



PLANTA DE ALUMBRADO — C1 — E: 1/50

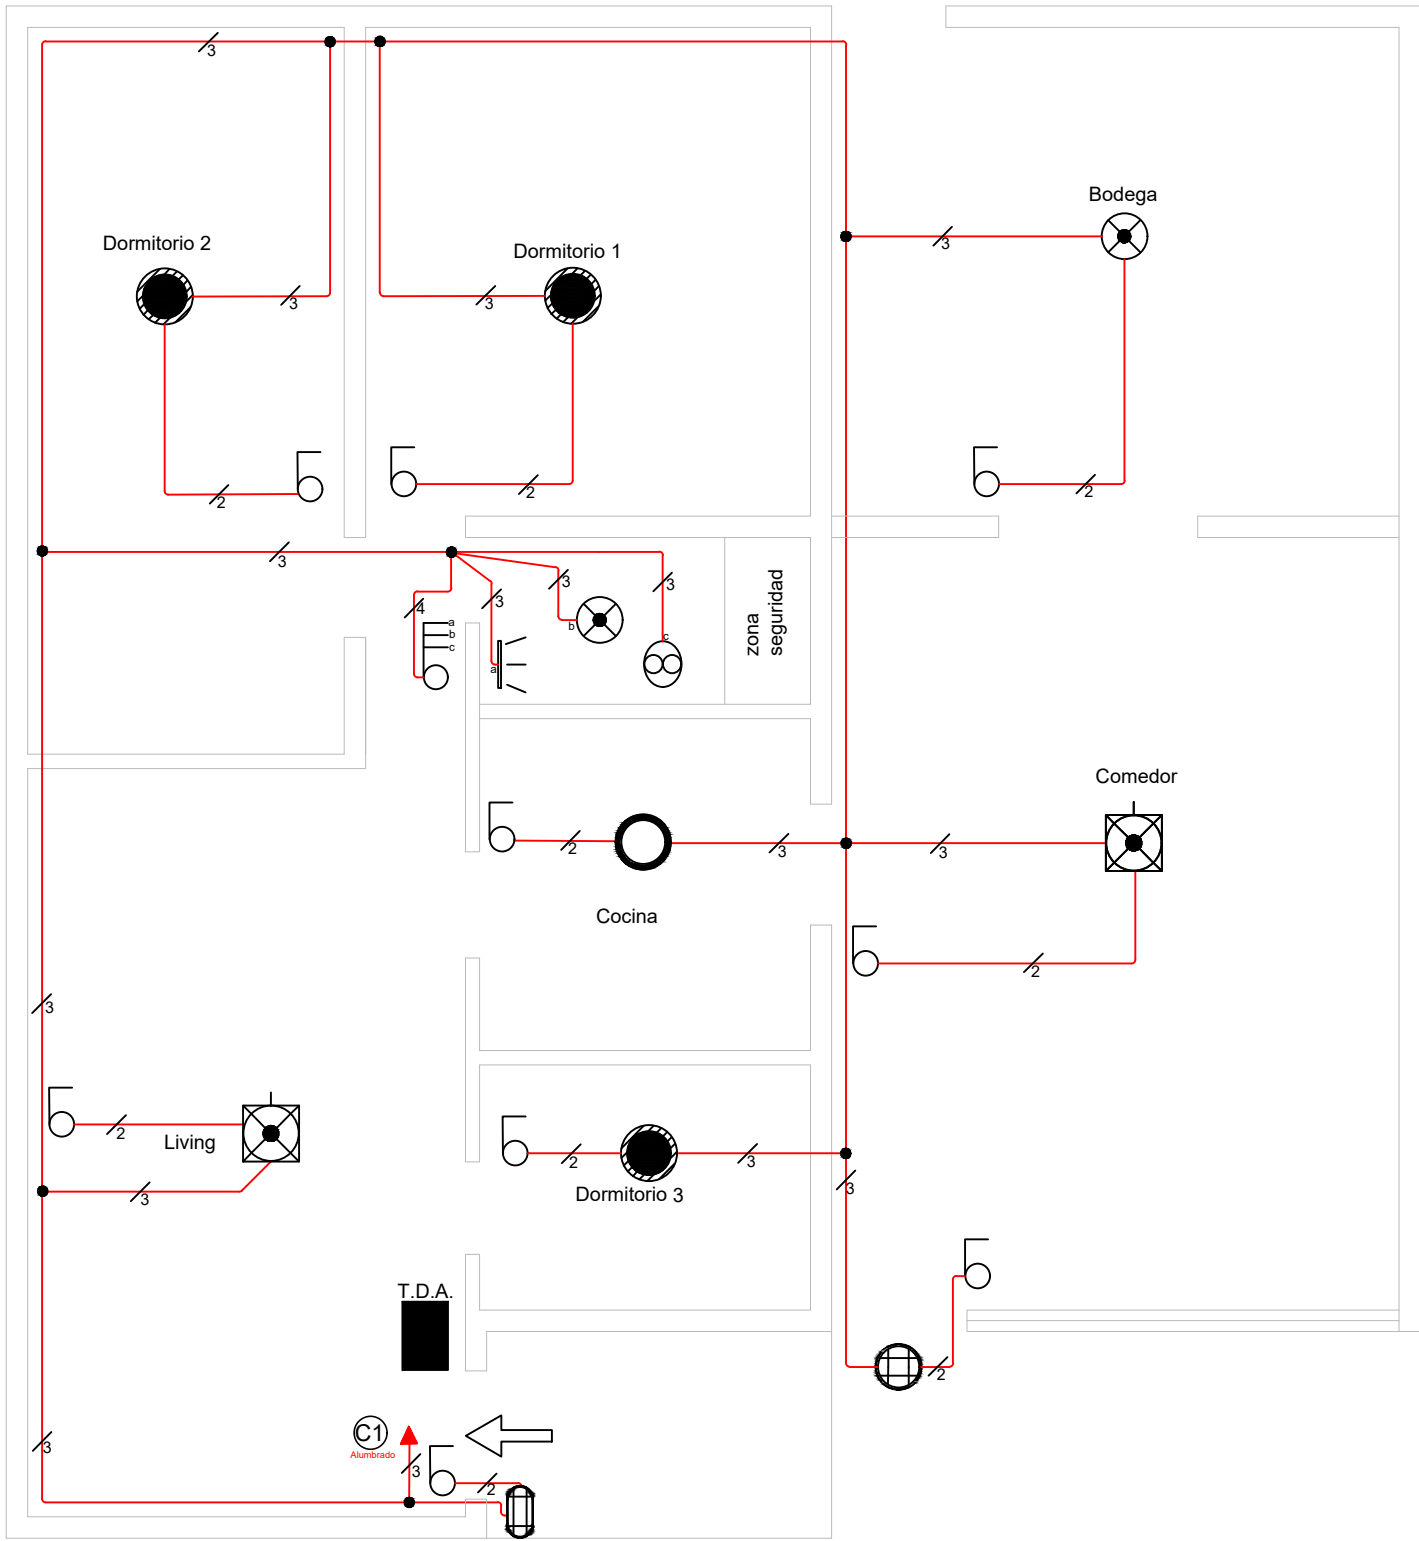

PLANTA DE ENCHUFES — C2 y C3 — E: 1/50

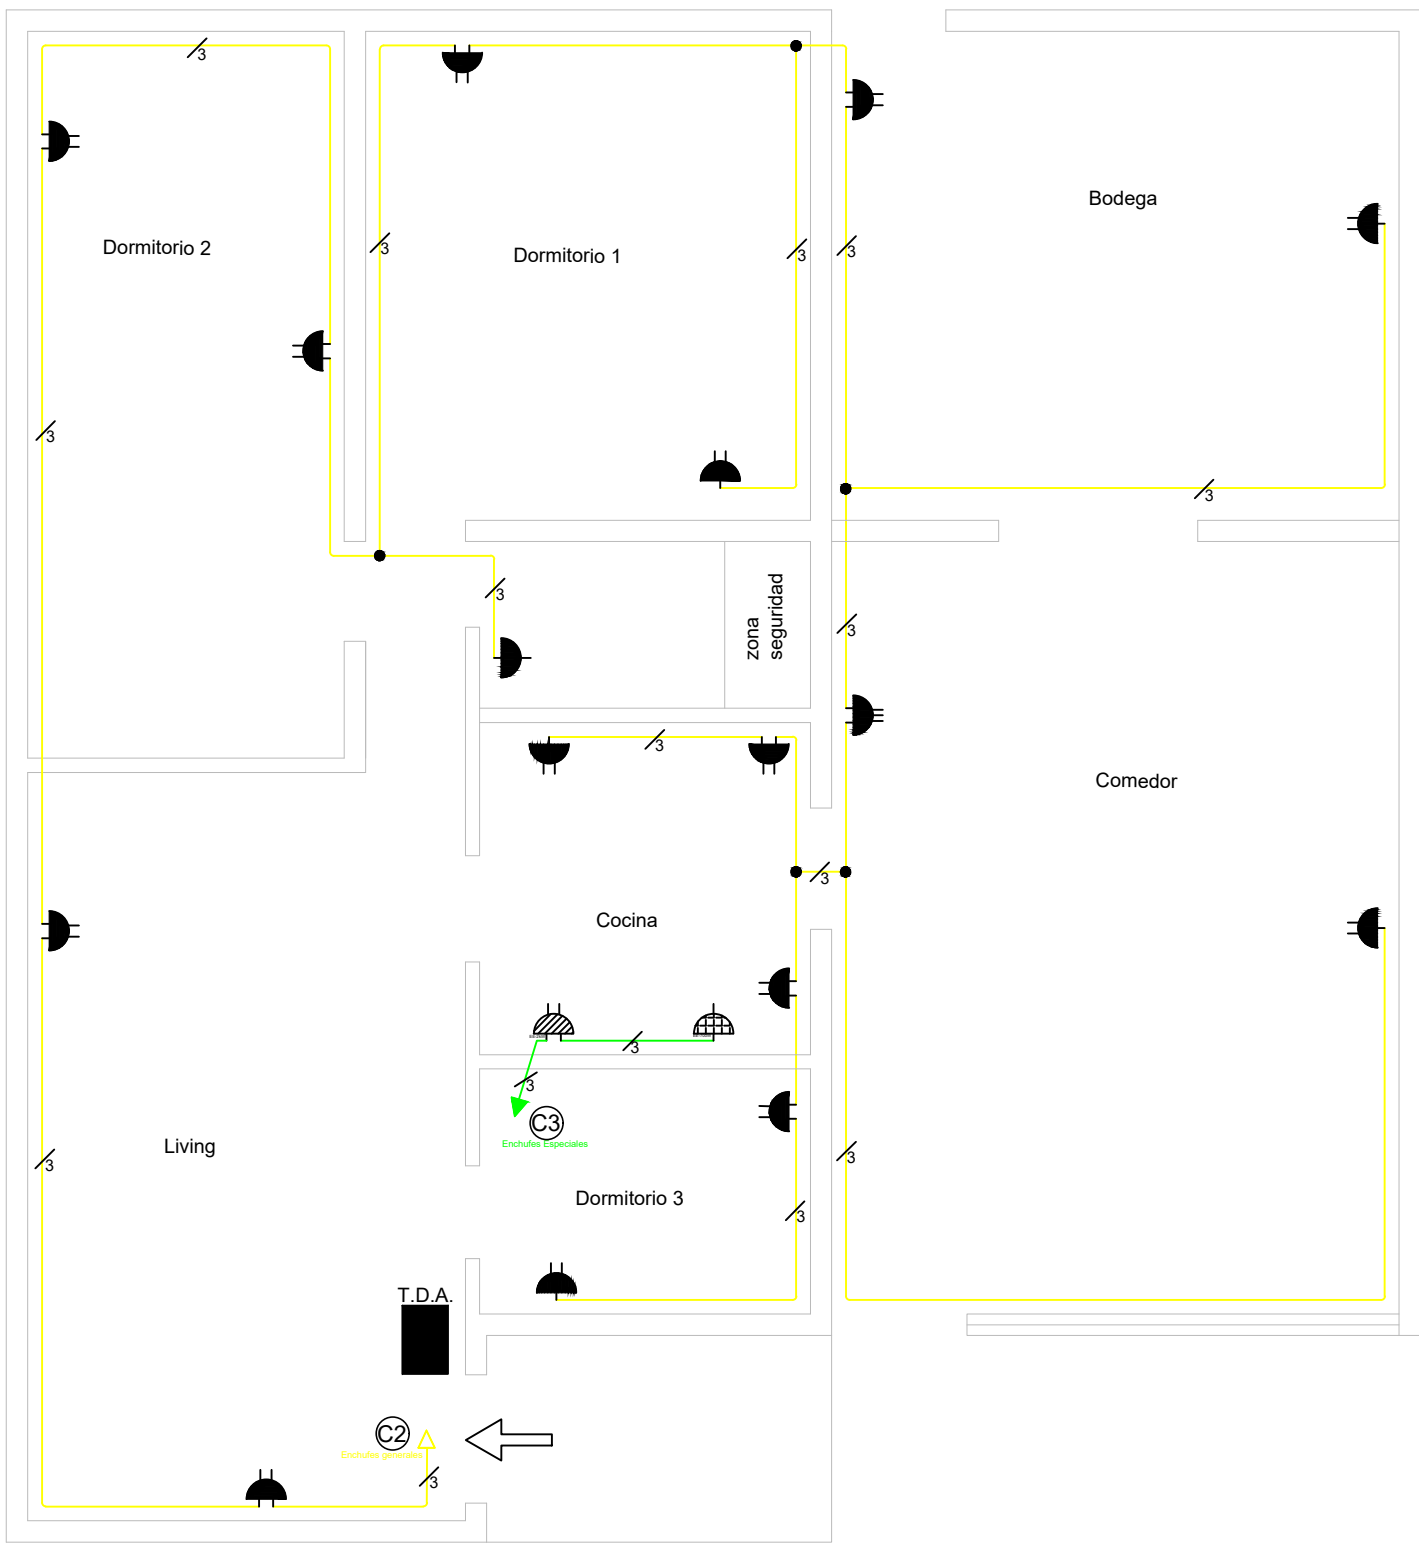

CÁLCULO DE ALIMENTADOR Y PROTECCIÓN GENERAL

Datos:
Ptotal = 7.474 kW
V = 220 V
L = 50 m
Alimentador seleccionado: Cu 10 mm²

Corriente total:
 $I = P / V$
 $I = 7474 / 220 = 33.97 \text{ A}$

Protección general:
Se selecciona IGA 2x40A, curva C, Icn 10 kA.


Caída de tensión:
 $\Delta V = (2 \times L \times I \times \rho) / S$
 $\Delta V = (2 \times 50 \times 33.97 \times 0.018) / 10$
 $\Delta V = 6.11 \text{ V}$

$\% \Delta V = (6.11 / 220) \times 100 = 2.78 \%$

Conclusión:
Se adopta alimentador Cu 10 mm² en canalización subterránea, con protección general 2x40A.

DIAGRAMA UNILINEAL

TDA

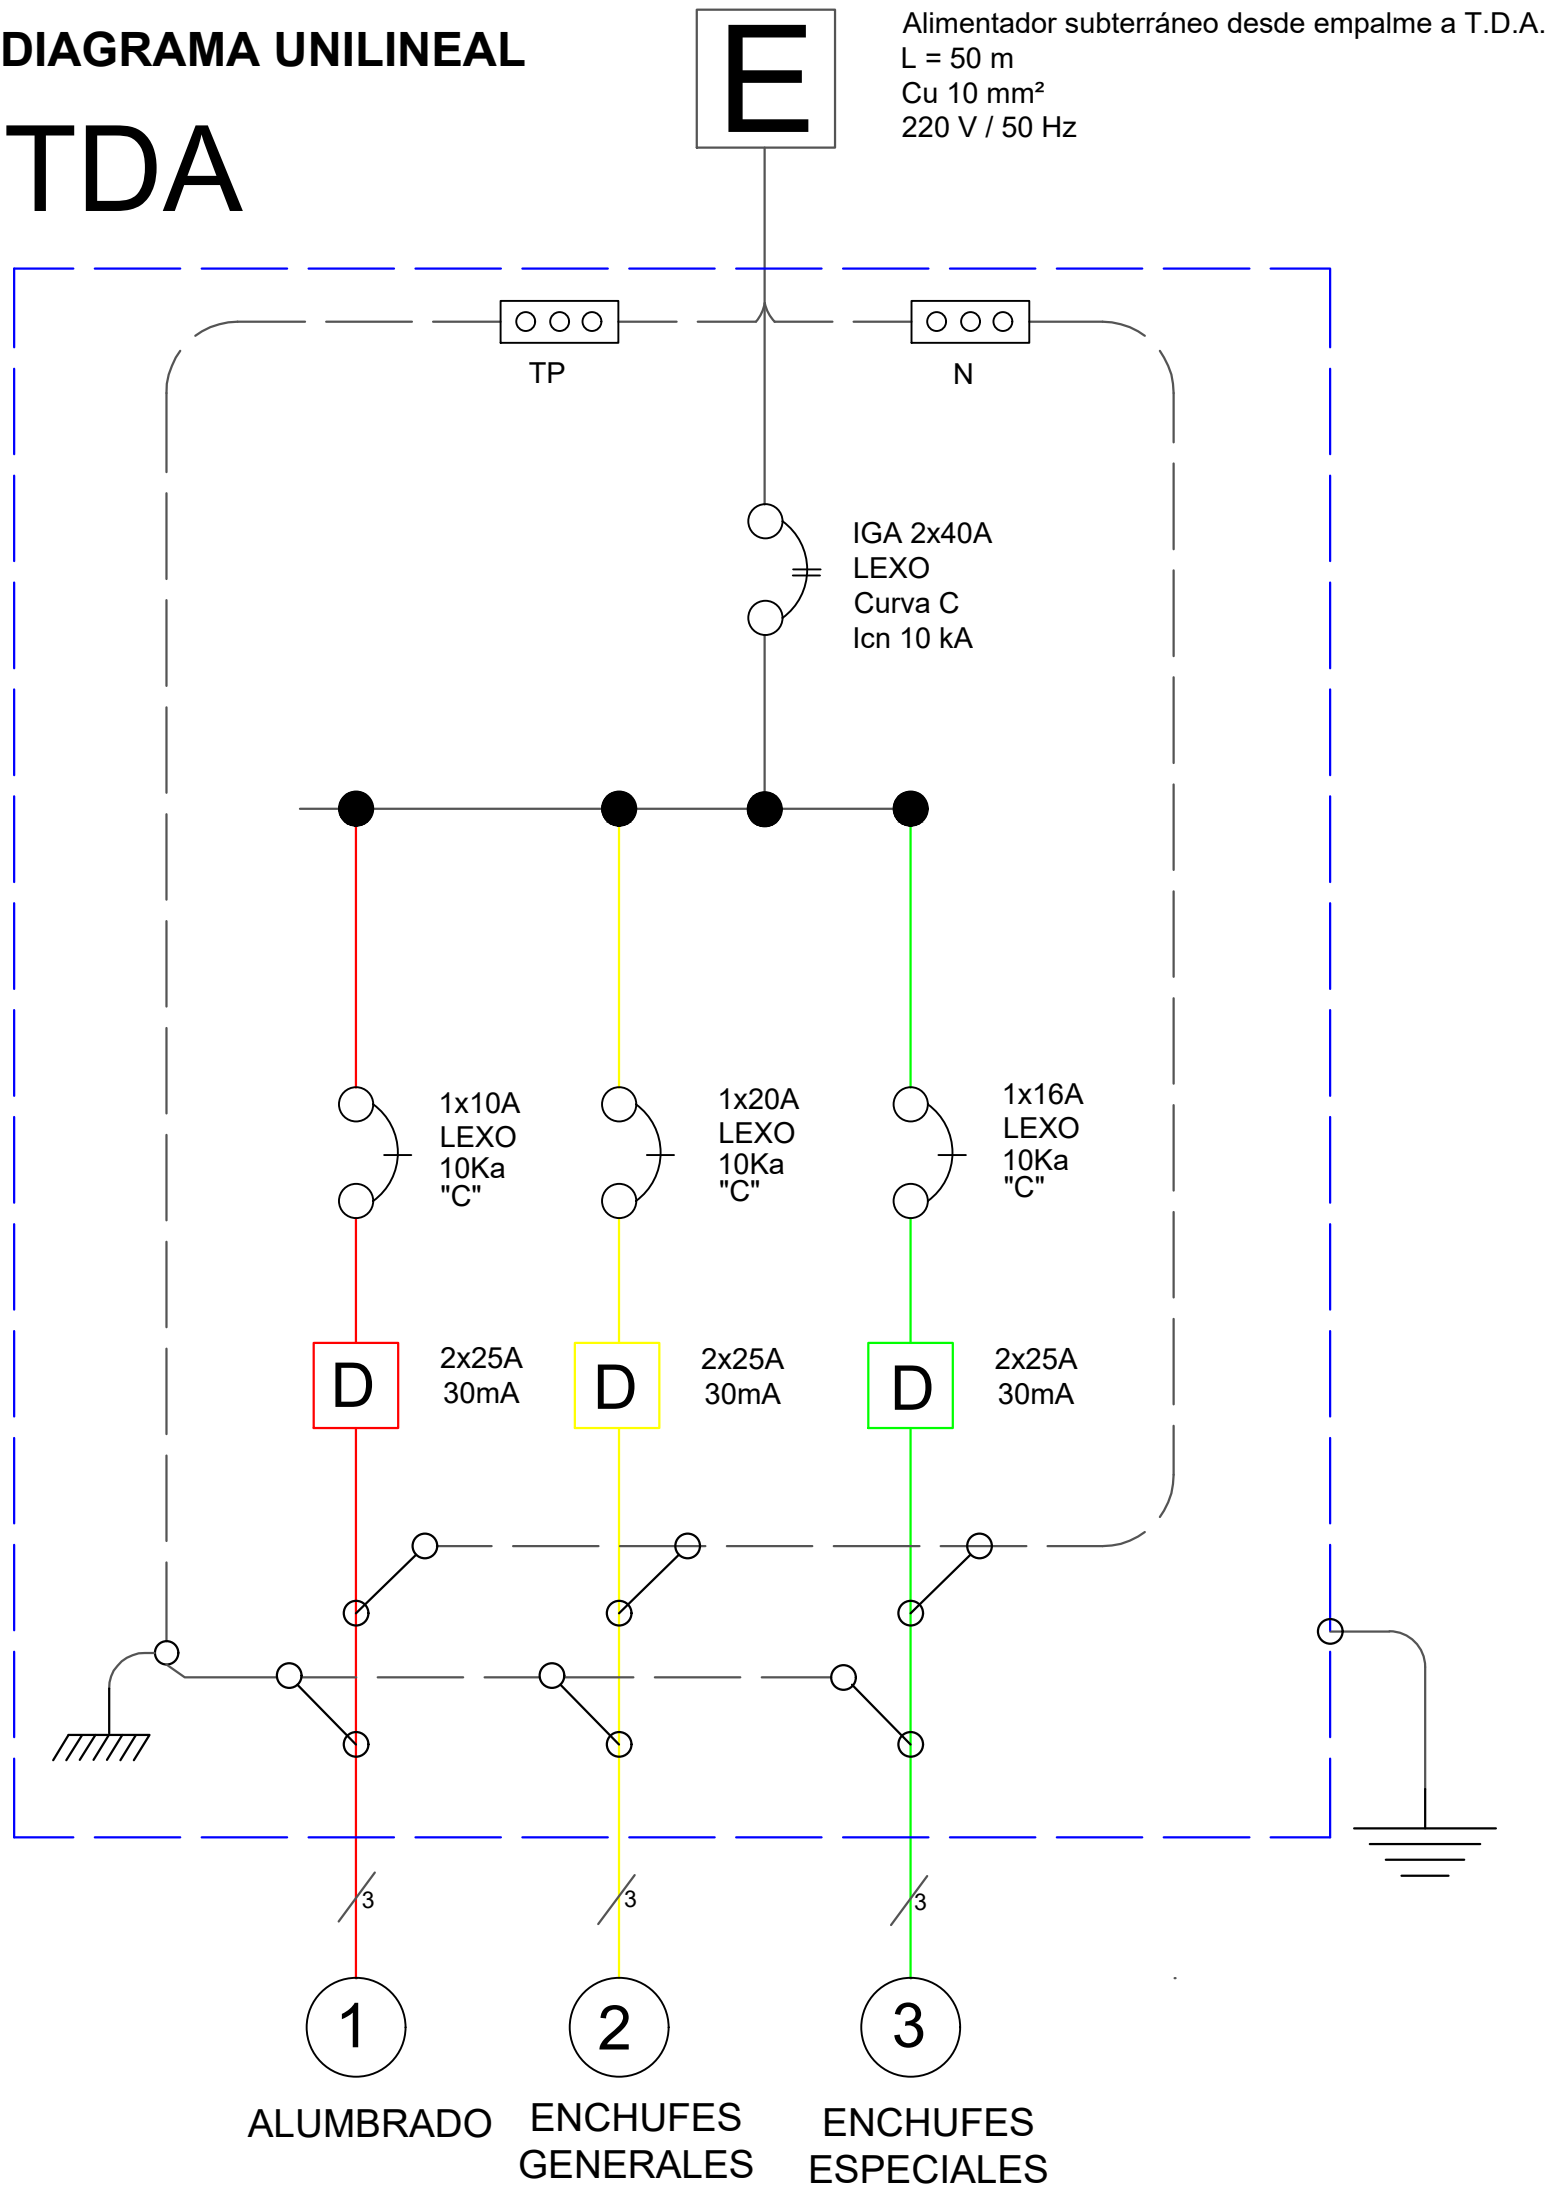

SIMBOLOGIA:

- PORTA LAMPARA 100W
- CAJA DE DERIVACION
- INTERRUPTOR 9/12
- INTERRUPTOR 9/32
- CANALIZACIÓN EMBUTIDA tpr 1/2 Ø
- TABLERO DE ALUMBRADO
- APLIQUE TIPO TORTUGA EXTERIOR 60 W
- FOCO EXTERIOR TIPO TORTUGA ANOLA DM185 E27 40 W
- LAMPARA DE TECHO COLGANTE TIPO JAULA E27, 3 x 60 W

- PLAFÓN LED REDONDO SOBREPUESTO 24 W
- PLAFÓN LED RUSTICO SOBREPUESTO 24 W
- LUZ ESPEJO 6W
- EXTRACTOR DE AIRE TECHO/PARED 4" DE 12 W
- ENCHUFE SIMPLE DE ALUMBRADO
- ENCHUFE DOBLE DE ALUMBRADO
- ENCHUFE TRIPLE
- ENCHUFE ESPECIAL 700W
- ENCHUFE ESPECIAL 2kW

- EMPALME
- PROTECTOR DIFERENCIAL
- PROTECTOR TERMOMAGNETICO MONOFÁSICO
- BARRA DE Cu PARA NEUTRO Y TIERRA PROTECCIÓN
- TOMA TIERRA SERVICIO
- TOMA TIERRA PROTECCIÓN
- REPRESENTA NUMERO DE CIRCUITO

NOTA: LOS MATERIALES UTILIZADOS EN ESTA INSTALACIÓN QUE REQUIERAN CERTIFICACIÓN, DEBERÁN CONTAR CON SU RESPECTIVO CERTIFICADO DE APROBACIÓN .

CUADRO DE DISTRIBUCIÓN DE CARGAS

DESIGNACIÓN TABLERO	CTO. N°	Porta Lámparas 100W	Aplicque tortuga exterior IP65 60 W	Foco exterior tortuga Ancla IP65 40 W	Lámpara colgante tipo jaula E27 3 x 60 W 180 W	Plafón LED Rustico/Redondo 24 W	Luz espejo de baño 6 W	Extractor aire techo/pared 4" 12 W	Enchufe simple de alumbrado 250 W	Enchufe doble de alumbrado 250 W	Enchufe triple de alumbrado 250 W	Enchufe especial cocina 700 W	Enchufe especial cocina 2 kW	TOTAL CENTROS	POTENCIA (kW)	I (A)	PROTECCION		CANALIZACION		UBICACION
																	DISYUNTOR	DIFERENCIAL	CONDUCTOR	DUCTO tp	
TDA	1	2	1	1	2	4	1	1						12	0.774 kW	3.52 A	1x10A	2x25A 30mA	1,5mm² H07V-K	tpr 1/2" 10'	Toda la casa
	2								1	14	1			16	4.000 kW	18.18 A	1x20A	2x25A 30mA	2,5mm² H07V-K	tpr 1/2" 10'	Living/Estar, dormitorios, baño, cocina, comedor y bodega
	3											1	1	2	2.700 kW	12.27 A	1x16A	2x25A 30mA	2,5mm² H07V-K	tpr 1/2" 10'	Cocina
TOTAL	3	2	1	1	2	4	1	1	1	14	1	1	1	30	7.474 kW	33.97 A					Total TDA

UBICACIÓN	INSCRIPCIÓN S.E.C.		PROYECTO DE INSTALACIÓN ELÉCTRICA RESIDENCIAL	
	INSCRIPCIÓN S.E.C.: N/A — PROYECTO ACADÉMICO		COMUNA: Pte. Alto CALLE: Concha y Toro Esq. San Carlos	LAMINA 01/01 ESCALA: 1:50 FECHA: JUL/2026 OTROS DATOS: Sistema monofásico 220 V / 50 Hz Alimentador subterráneo Empalme: 1.6A, L=50 m
			PROPIETARIO: Rosendo Muñoz	INSTALADOR: Maurizio Caballero
			FIRMA RUT .	FIRMA LICENCIA O TÍTULO: Estudiante PEI1108 DOMICILIO COMERCIAL: Proyecto académico TELÉFONO: +569 23927777